
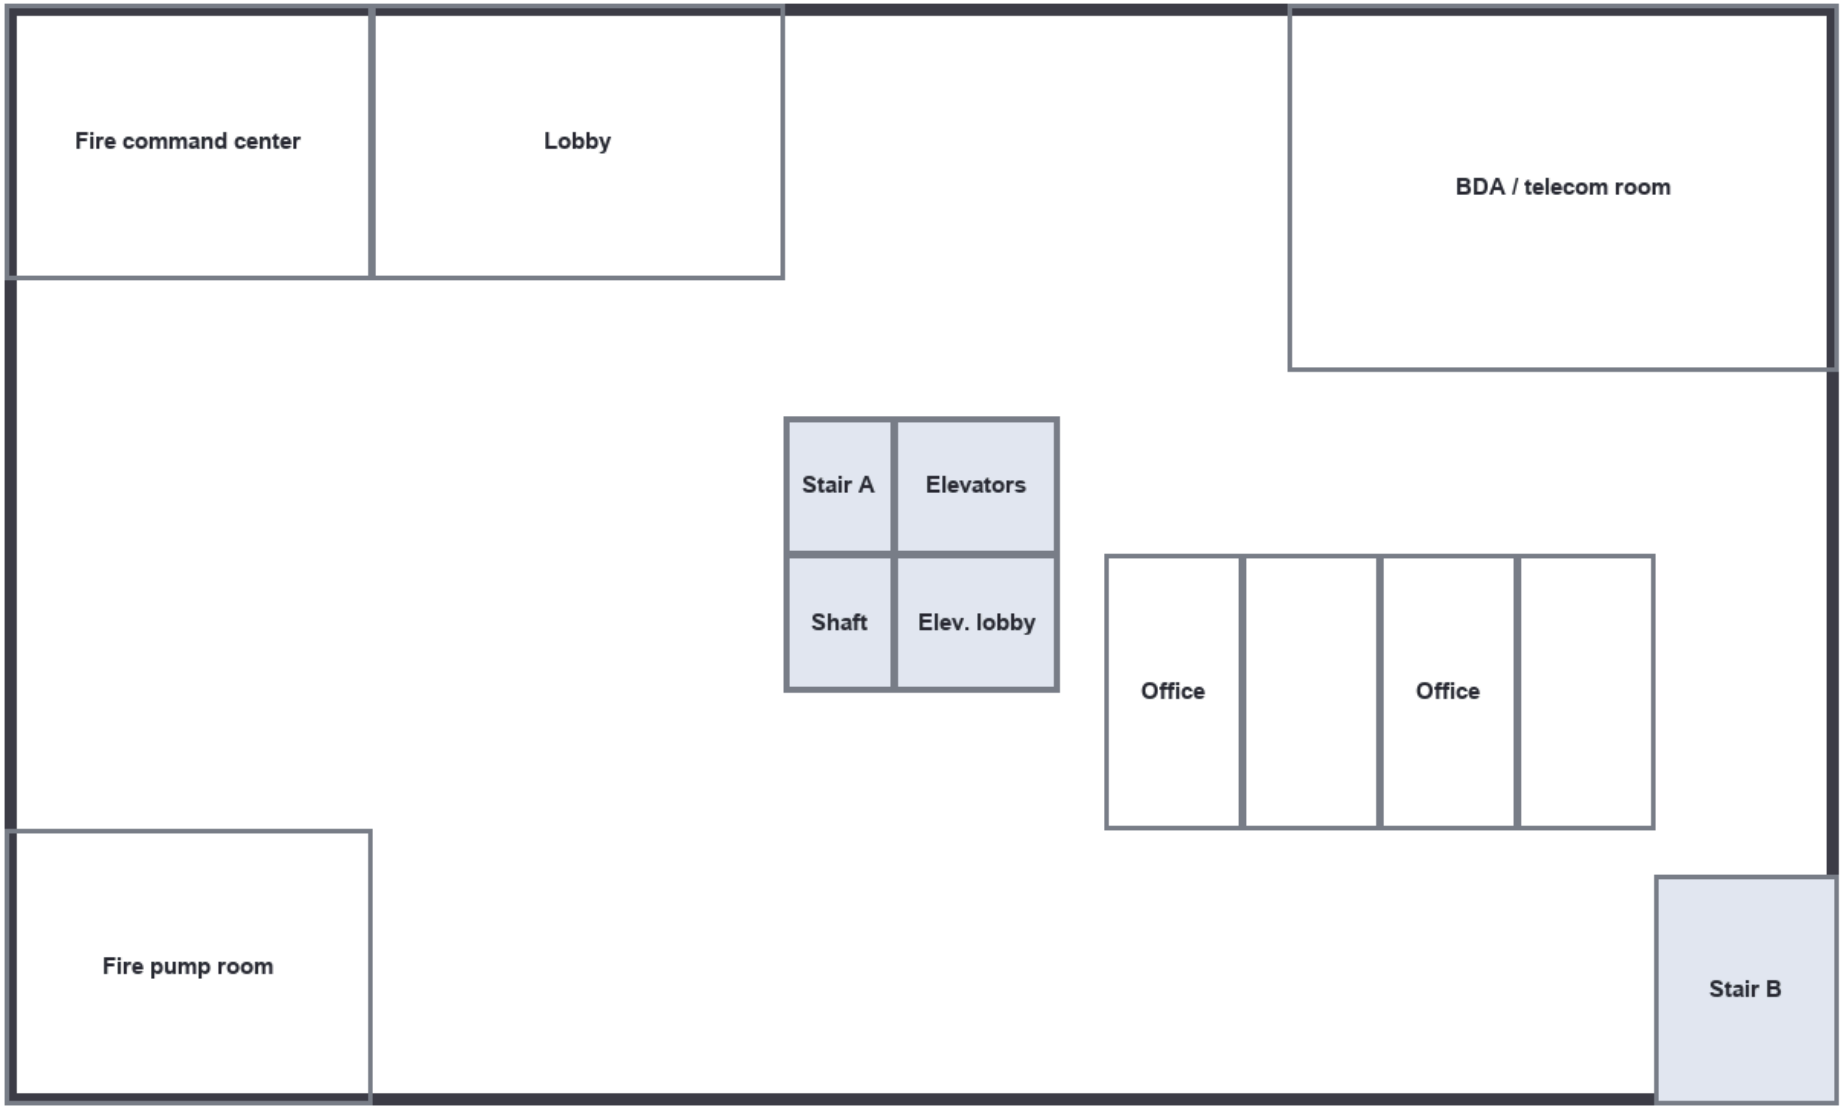


Example office building - Floor 1 (fictional plan for the RF Recon DAS example)

200 ft x 120 ft. Not a real building. Low-E glass curtain wall; concrete core.


50 ft

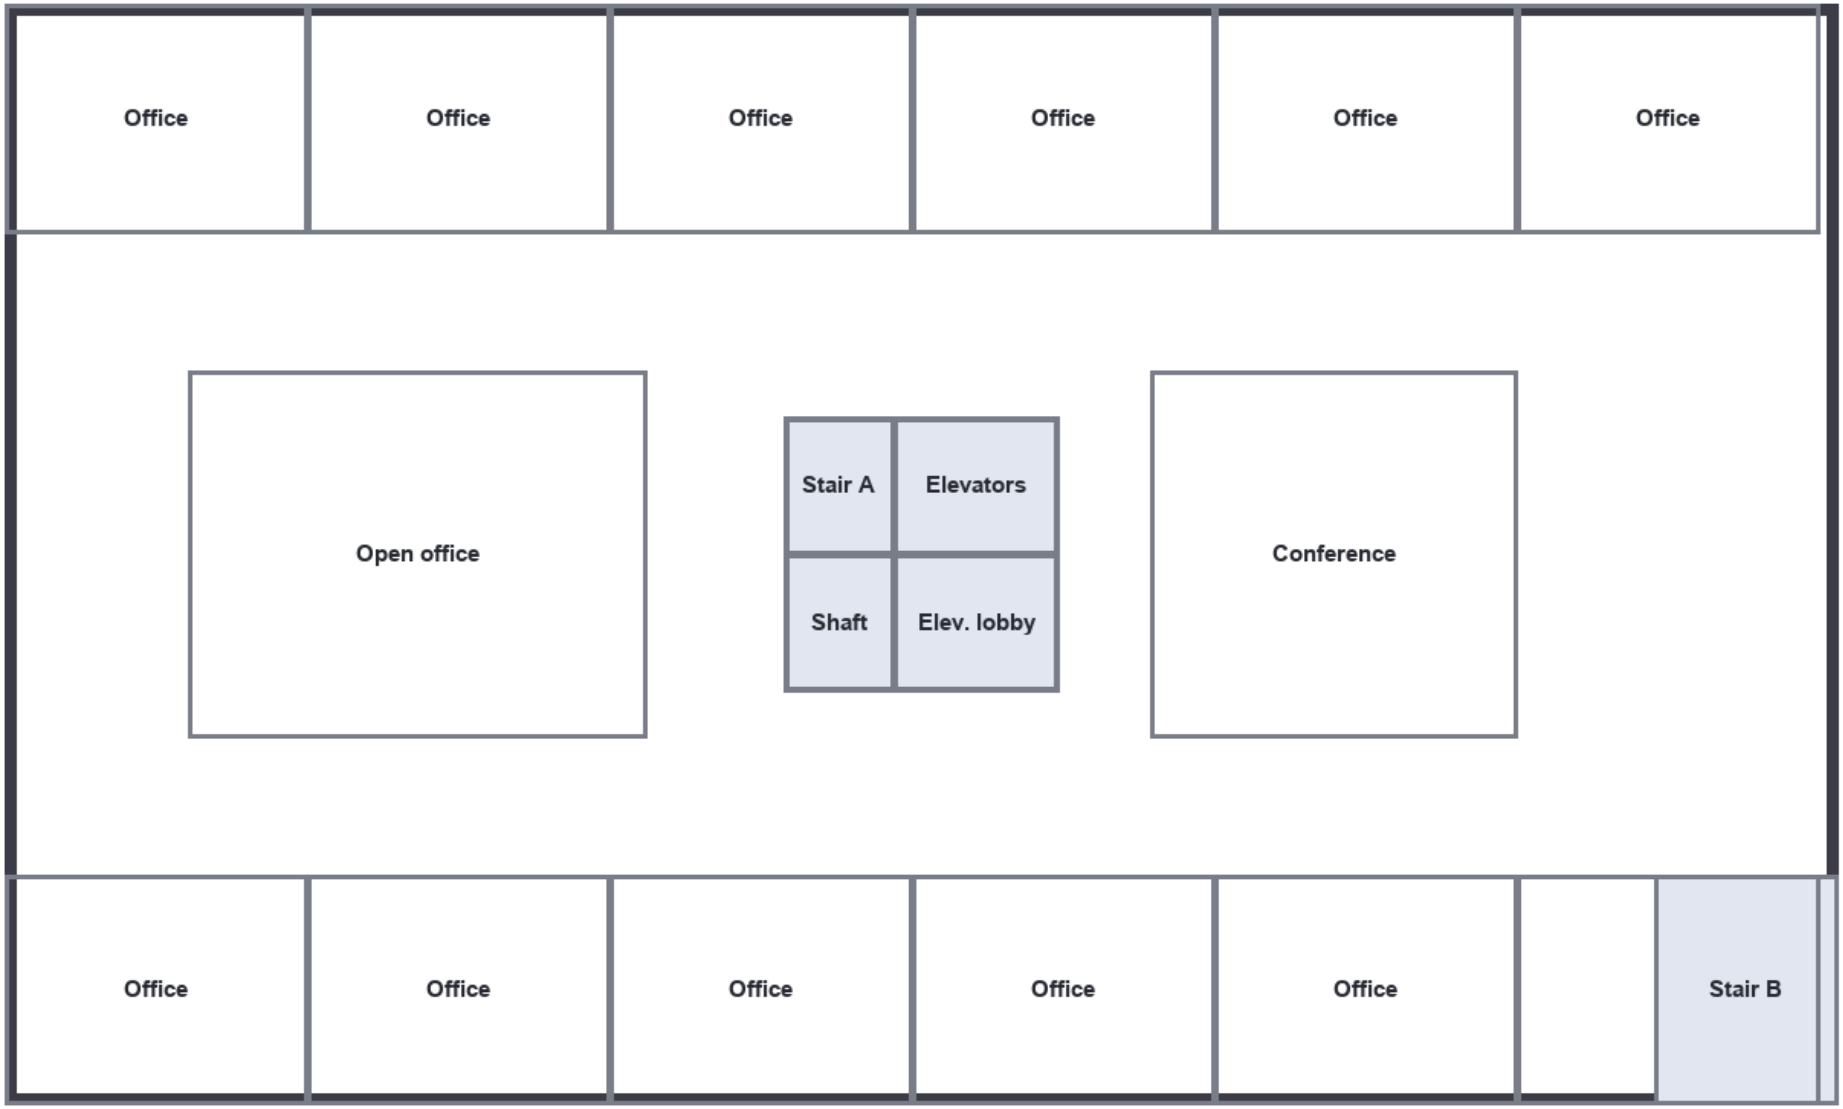

Example office building - Floor 2 (fictional plan for the RF Recon DAS example)

200 ft x 120 ft. Not a real building. Low-E glass curtain wall; concrete core.

50 ft

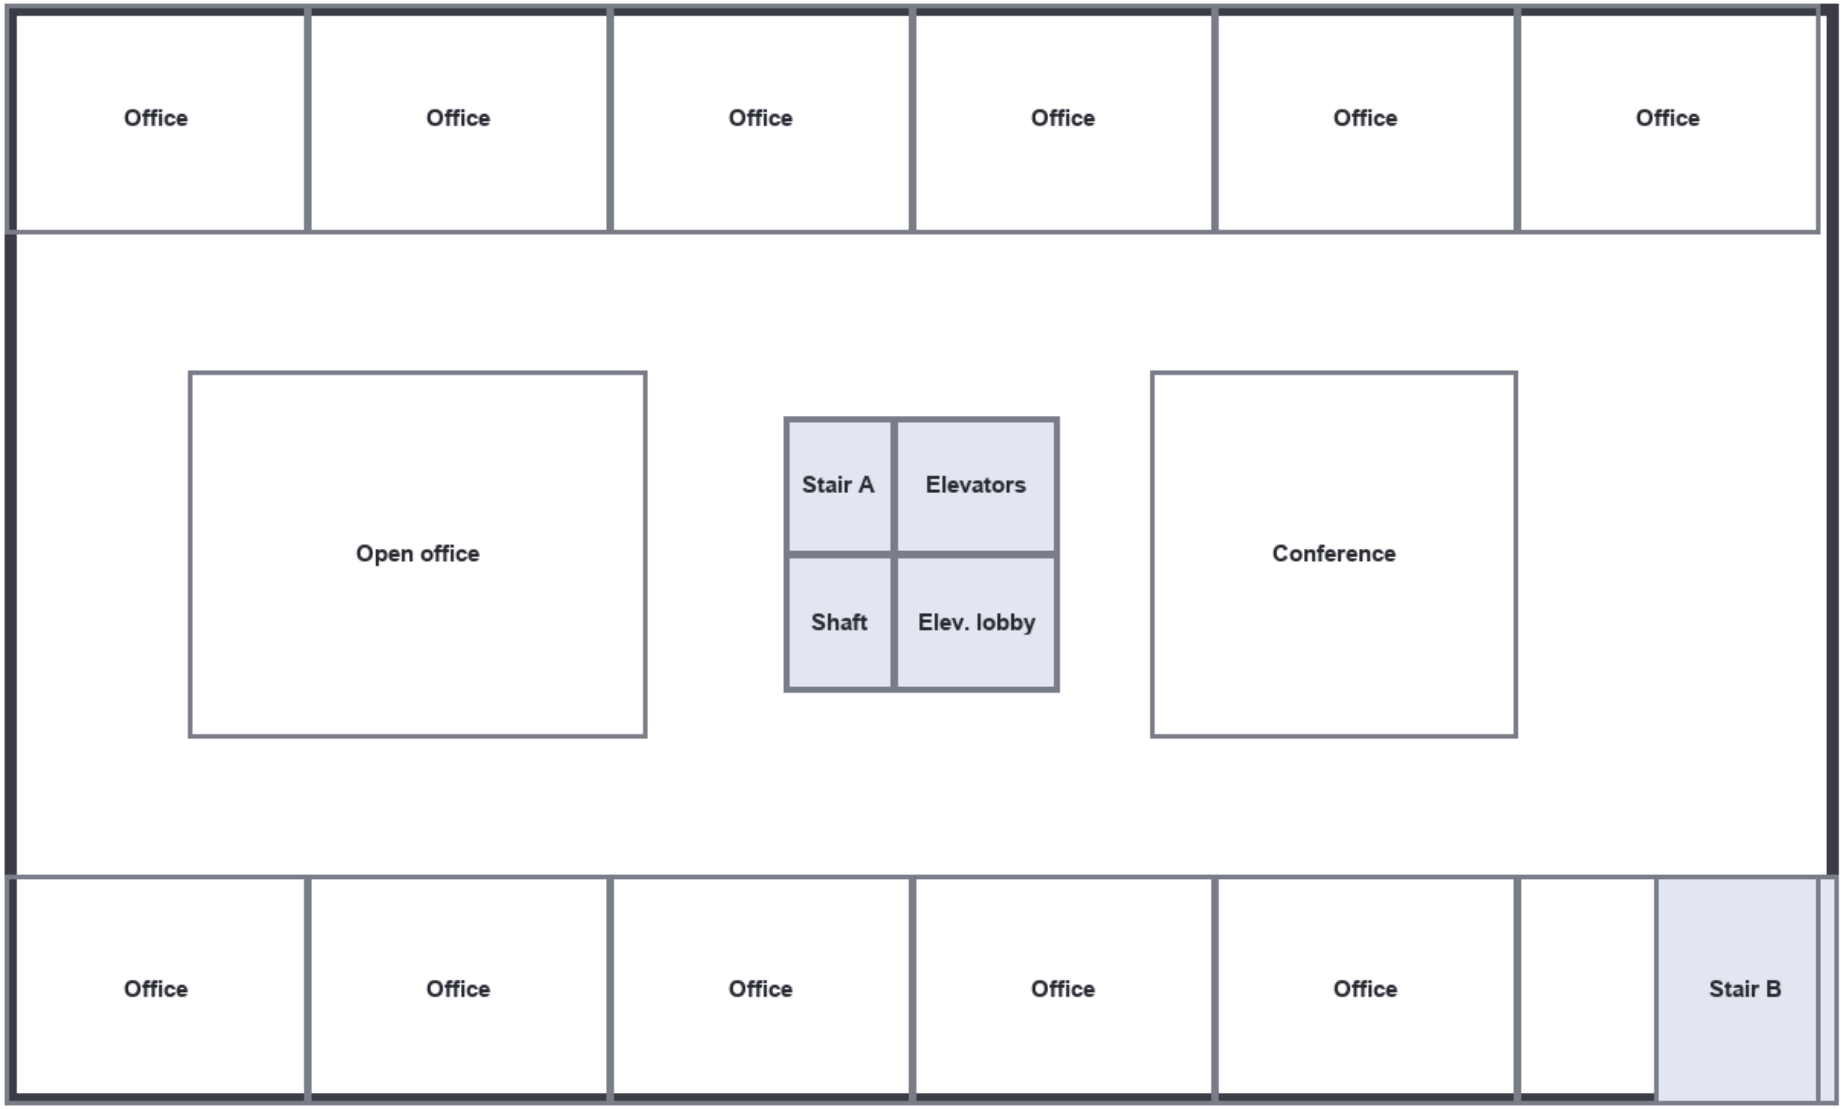

Example office building - Floor 3 (fictional plan for the RF Recon DAS example)

200 ft x 120 ft. Not a real building. Low-E glass curtain wall; concrete core.

50 ft